
BUILDING A / COMPREHENSIVE DETAIL PLAN

INFORMATION / CURATION / CLINIC / BINDING

01 / FLOOR PLAN

A1 / SCALE 1:100 / UNITS mm

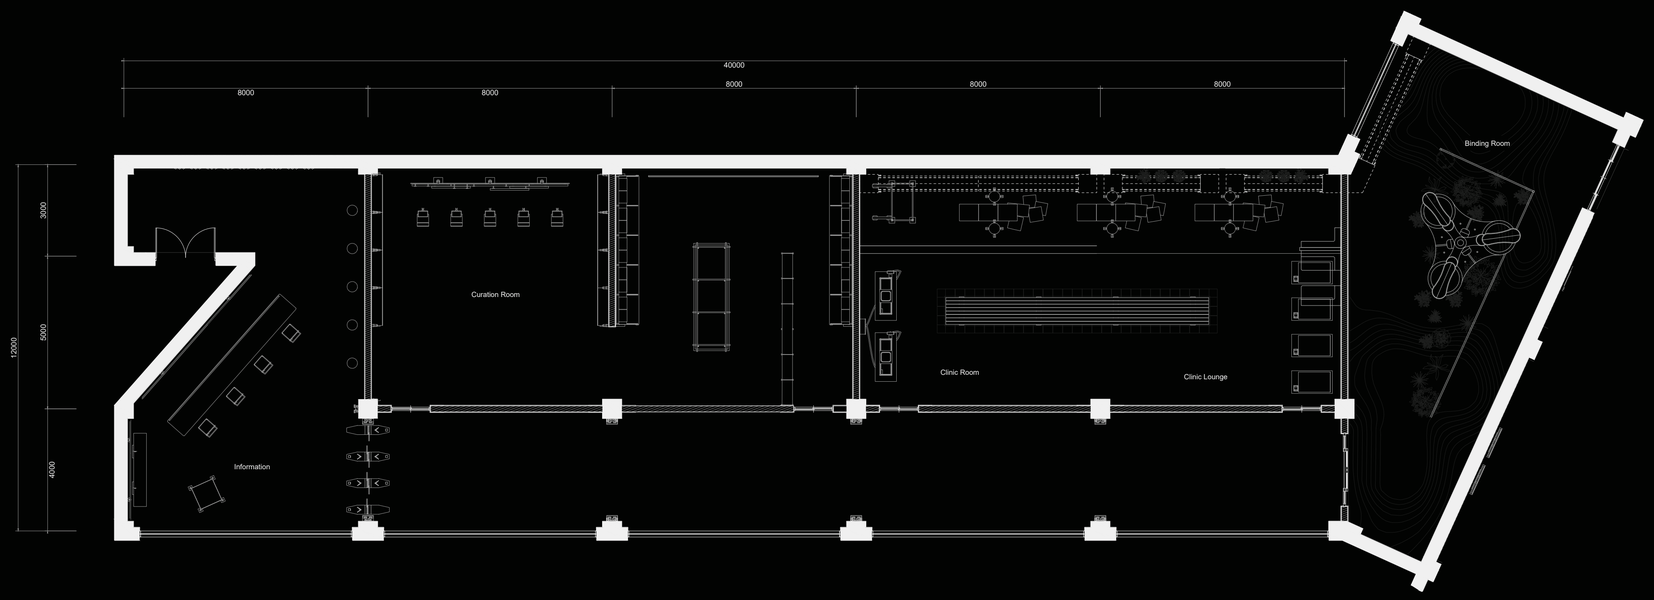

GRAPHIC SCALE / m

0 2 6 10

02 / SPATIAL PROGRAM

NO.	SPACE / ELEMENT
01	Information
02	Curation Room
03	Clinic Room
04	Clinic Lounge
05	Binding Room

SOURCE / DETAIL PLAN R26 / 2026.10.20

03 / DIMENSION REGISTER

mm

REFERENCE	DIMENSION
X / Overall dimension chain	40000
X / Typical bay	8000
Y / Overall dimension chain	12000
Y / Segment 01	3000
Y / Segment 02	5000
Y / Segment 03	4000


Dimension chains shown in the source plan. Values retained without reinterpretation.

BUILDING B / COMPREHENSIVE DETAIL PLAN

PRINTING / HEATING / STORAGE / INCUBATING / INOCULATION / PICKUP / LOUNGE

01 / FLOOR PLAN

A1 / SCALE 1:100 / UNITS mm

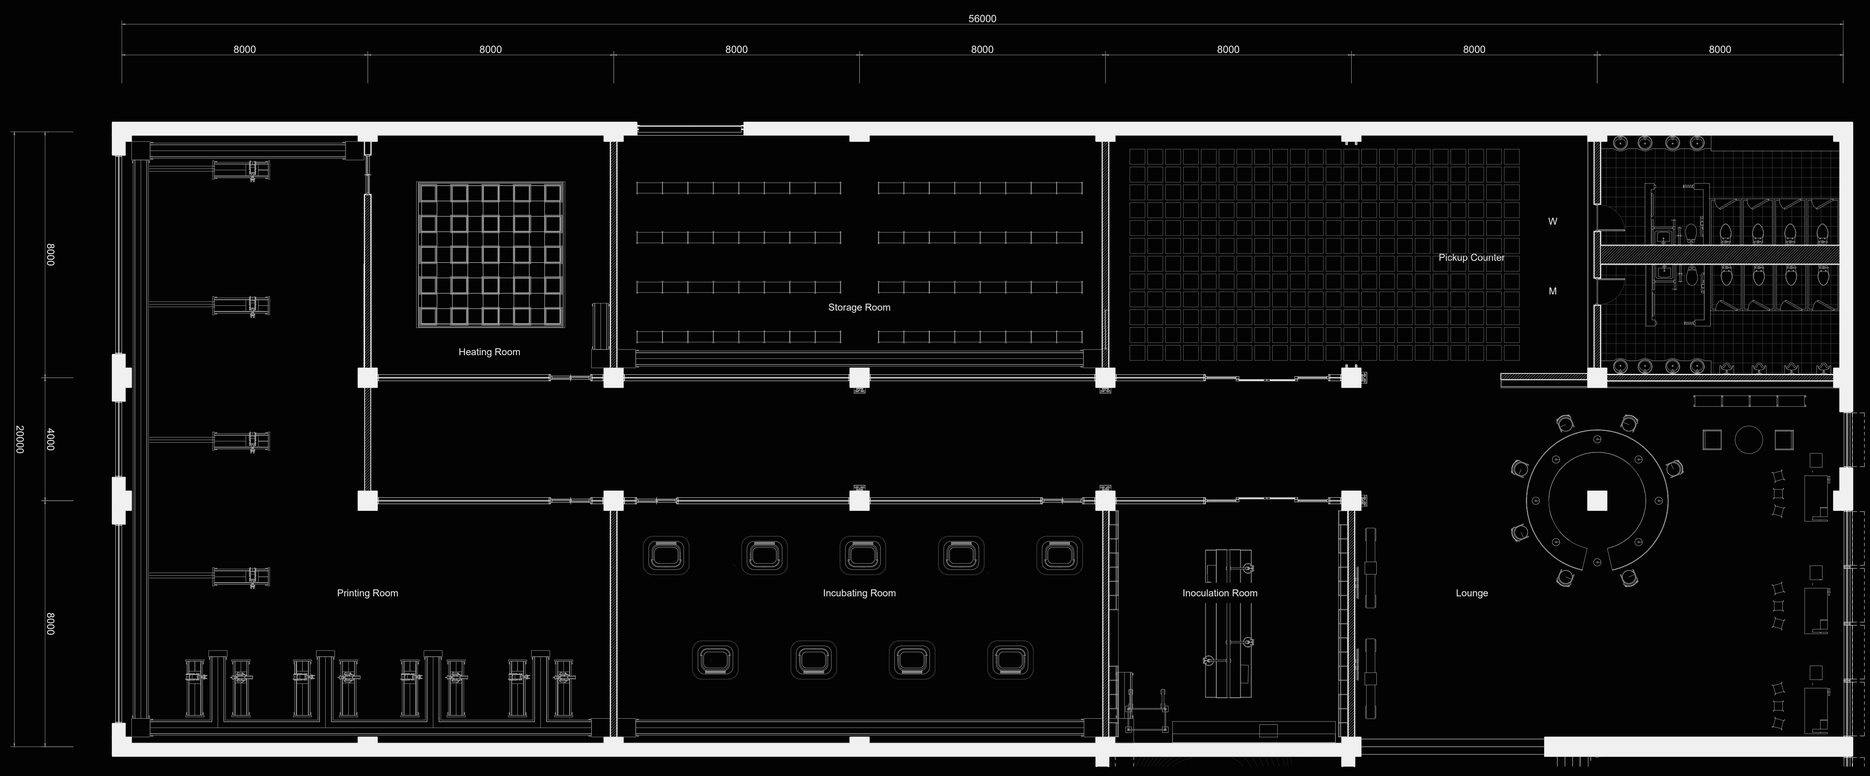

GRAPHIC SCALE / m

0 2 6 10

02 / SPATIAL PROGRAM

NO.	SPACE / ELEMENT
01	Printing Room
02	Heating Room
03	Storage Room
04	Incubating Room
05	Inoculation Room
06	Pickup Counter
07	Lounge

SOURCE / DETAIL PLAN R26 / 2026.10.20

03 / DIMENSION REGISTER

mm

REFERENCE	DIMENSION
Printing Room	15900
Heating Room	7800 / 7800
Storage Room	15800 / 7400
Incubating Room	15820
Inoculation Room	7800
Pickup Counter	15800 / 19650
Lounge	15925 / 7400


Interior measurements at the locations documented in the source plan.

BUILDING C / WORKSHOP DETAIL PLAN

WORKSHOP / MOBILE PARTITIONS / LANDSCAPED CORRIDOR / TOILETS

01 / FLOOR PLAN

A1 / SCALE 1:100 / UNITS mm

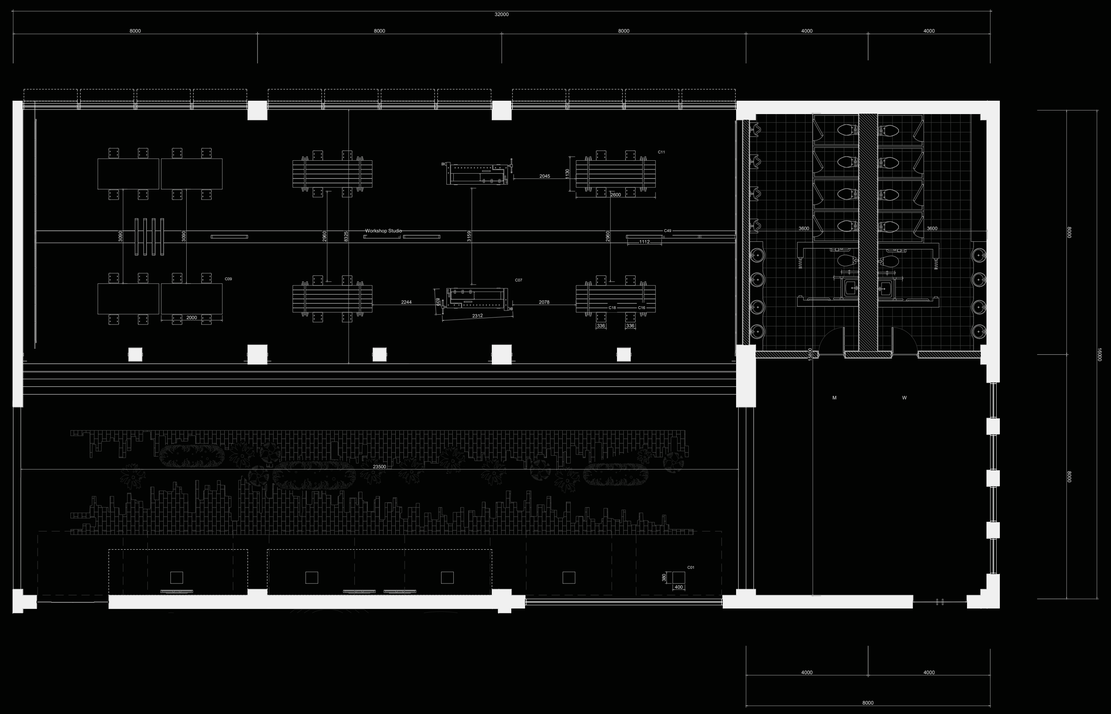

GRAPHIC SCALE / m

0 2 6 10

02 / SPATIAL PROGRAM

NO.	SPACE / ELEMENT
01	Workshop Studio
02	Landscaped Corridor
03	Toilets
04	Worktables
05	Mobile Partition Panels
06	Workshop Benches
07	Stools

SOURCE / DETAIL PLAN R26 / 2026.10.20

03 / DIMENSION REGISTER

mm

REFERENCE	DIMENSION
C11 / Worktable	2600 x 1130
C09 / Worktable	2000 x 1000
C07 / Worktable	2312 x 839
C01 / Workshop Bench	400 x 380
C49 / Mobile Partition Panel	1112 x 94
C16 / Stool	336 x 336
C18 / Stool	336 x 328

Representative furniture overall dimensions documented in the source plan.